Villa Mercedes 16 de noviembre de 2017.-

VISTO:

EL EXPEDIENTE CUDAP: UVM Nº 0001310/2017

CONSIDERANDO:

Que mediante el expediente de referencia se informa las condiciones generales de higiene, seguridad y protección contra incendios de acuerdo a lo detallado por el Ingeniero Sergio PASCUAL en los edificios de España Nº80, Balcarce y España, Sala de Computación y Laboratorio en calles Guayaquil y Tucumán.

Que en el informe se tiene en cuenta los siguientes ítems: vías de escape y salidas de emergencia, iluminación de emergencia, señalización de vías de escape, instalaciones eléctricas y riesgos eléctricos, extintores portátiles, accesibilidad de equipos de emergencia y rescate, pisos, techos, paredes y estructura general, almacenamiento y uso de productos químicos, instalaciones de gas y calefactores, provisión de agua potable y sanitarios, orden y limpieza.

Que Secretaría Academica solicita un plan de mejora en las condiciones generales de higiene, seguridad y protección contra incendios de los edificios, de los cuales hace uso esta Universidad, en carácter urgente; y su protocolización correspondiente.

Que el Ingeniero Arnoldo Domingo PUCCI especialista en seguridad e higiene eleva un informe de planificación de mejoras en los edificios de España Nº80, Balcarce y España, Sala de Computación y Laboratorio en calles Guayaquil y Tucumán.

Que Rectorado presta acuerdo favorable, solicitando la emisión de actos administrativos pertinentes.

Que la presente medida se realiza en virtud de lo establecido en el artículo 49 de la LEY 24.521 de EDUCACION SUPERIOR.

Por ello y en uso de sus atribuciones,

EL RECTOR ORGANIZADOR DE LA
UNIVERSIDAD NACIONAL DE VILLA MERCEDES
RESUELVE:

ARTICULO 1º.- PROTOCOLIZAR el informe de planificación de mejoras y protección contra incendios en los edificios de España Nº80, Balcarce y España, Sala de Computación y Laboratorio en calles Guayaquil y Tucumán en los cuales se desarrollan actividades pertenecientes a la Universidad Nacional de Villa Mercedes.

ARTICULO 2°.- Notifíquese, insértese en el Libro de Resoluciones y archívese.

RESOLUCION R. N° 000893/2017.

C: GAB

Mg. Daniel Enrique ARDISSONE
Secretaría Academica y Posgrado
Universidad Nacional de Villa Mercedes

Dr. David Luciano RIVAROLA
Rector Organizador
Universidad Nacional de Villa Mercedes

ANEXO I
Corresponde Resolución R. Nº 000893/2017

Venido a esta Unidad de Gestión de Riesgo el expediente EXP-UVM:00001310/2017, se realiza el siguiente informe a los efectos de planificar las correcciones que a continuación se detallan y que se les asigna las siguientes prioridades:

PRIORIDAD 1: MENOS DE 30 Días

PRIORIDAD 2: ENTRE 30 Y 60 Días

PRIORIDAD 3: ENTRE 60 Y 90 Días

A continuación, se realiza el siguiente detalle de tareas a desarrollar, según los puntos del informe:

Items 1 del informe:

a. Referido al ancho de las vías de escape el mismo es un déficit estructural dado que es un edificio existente, siendo su modificación de solución una modificación de la distribución de aulas, la que sería una implementación a mediano plazo, quedando a criterio de la superioridad su implementación.
b. Se debería cambiar el sentido de apertura de las puertas según el sentido de la evacuación. **PRIORIDAD 2.**
c. Reparar barral antipánico en puerta de laboratorio sector ESTE. **PRIORIDAD 1.**
d. Se deberá adecuar las aulas al factor de ocupación que fija la normativa vigente, dado que la misma se encuentra superado. **PRIORIDAD 2.**
e. Construir escalera para habilitar salida de emergencia en el edificio de España 80. **PRIORIDAD 3.**

Dr. David Rivarola
Rector Organizador
Universidad Nacional de Villa Mercedes

Items 2 del Informe

a. Se deberán comprar y colocar 20 luces de emergencias. **PRIORIDAD 3.** (Ver planimetría adjunta)

Items 3 del Informe

a. Colocar los croquis de evacuación en todos los edificios. **PRIORIDAD 1.** (ver planimetría adjunta).
b. Confeccionar plan de emergencias y evacuación. **PRIORIDAD 3.**

Daniel Enrique Ardissone
Secretaría Académica
Universidad Nacional de Villa Mercedes

Items 4 del informe

a. Realizar medición de la puesta a tierra y continuidad de masas de todos los edificios según resolución SRT-900/2015. **PRIORIDAD 3.**
b. Realizar una revisión de todas las instalaciones eléctricas por profesional habilitado. **PRIORIDAD 2.**

Items 5 del Informe

a. Se deberán comprar 6 extintores tipo ABC de 5 kg, completos para el puesto (extintor, chapa baliza y señalización en altura). **PRIORIDAD 1.**

Items 7 del Informe

a. Realizar estudio de carga de fuego en todos los edificios. **PRIORIDAD 3.**

Items 8 del Informe

a. Realizar la reparación de las duchas y lavaojos del laboratorio. **PRIORIDAD 1.**
b. Reforzar la señalización indicada y poner las indicaciones en idioma español. **PRIORIDAD 1.**

Items 9 del Informe

a. Fijar anafe en el edificio de España 80. **PRIORIDAD 1.**
b. Confeccionar plano y relevamiento de instalación de gas por profesional habilitado. **PRIORIDAD 3.**
c. Reforzar señalización en el laboratorio. **PRIORIDAD 2.**

Items 10 del Informe

a. No existencia de número adecuado de sanitarios por el factor de ocupación, se deja a criterio de la superioridad la modificación del edificio para su cumplimiento.
b. Realizar la limpieza de los tanques y luego tener una frecuencia anual dejando el registro respectivo. **PRIORIDAD 1.**
c. Realizar un análisis físico químico anual y bacteriológico semestral del agua potable y solicitar al proveedor de bidones los respectivos análisis. **PRIORIDAD 1.**

Además, se deberá dar cumplimiento a todo lo sugerido en el mencionado informe. Se adjunta a la presente los planos de evacuación y de ubicación de extintores, luces de emergencias y cartelería de evacuación que oportunamente se enviaran a la oficina de acreditaciones para su impresión y colocación.

Sirva la presente de atenta nota

Villa Mercedes, 06 de Noviembre de 2017

Daniel Enrique Ardissone
Secretaría Académica
Universidad Nacional de Villa Mercedes

Dr. David Rivarola
Rector Organizador
Universidad Nacional de Villa Mercedes

CROQUIS DE EVACUACION - PLANTA BAJA


REFERENCIAS

Sentido de la Evacuación

Luces de Emergencias

Extintor Portátil

Punto de Encuentro

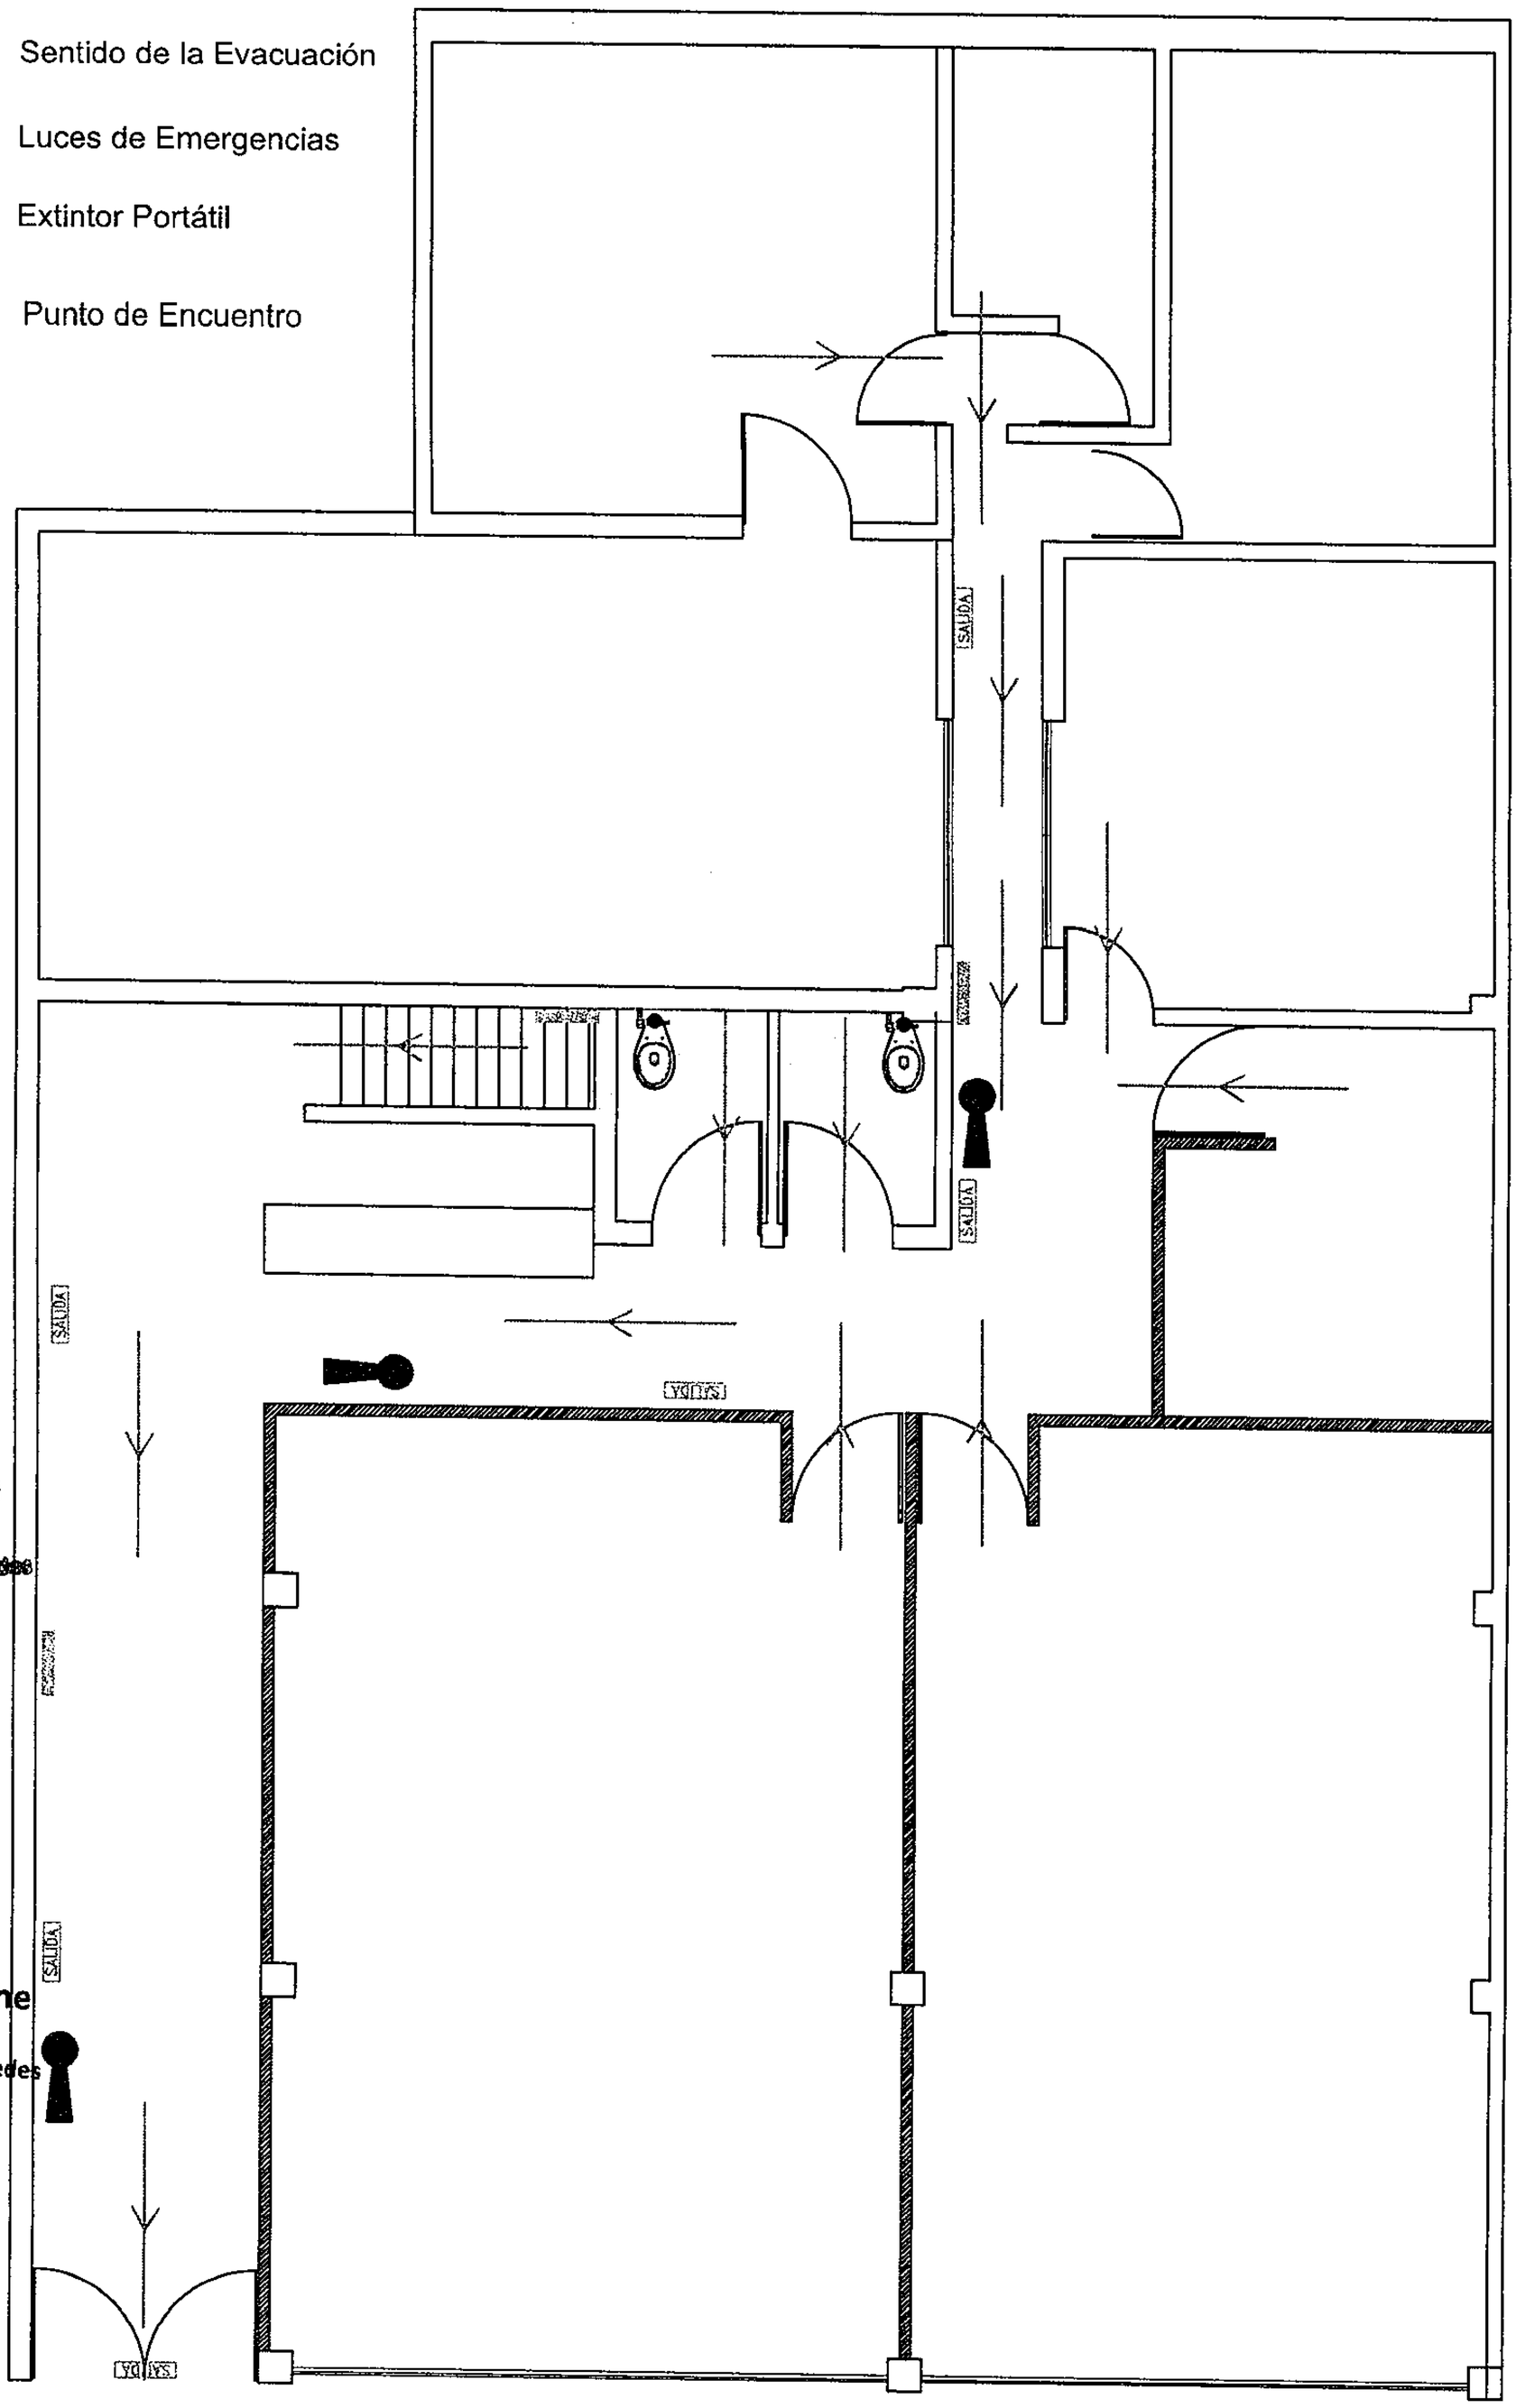

Dr. David Rivarola
Rector Organizador
Universidad Nacional de Villa Mercedes

Daniel Enrique Ardissone
Secretaría Académica
Universidad Nacional de Villa Mercedes

Corresponde Resolución R. Nº 000893/2017

CROQUIS DE EVACUACION - PLANTA BAJA


REFERENCIAS

Sentido de la Evacuación

Luces de Emergencias

Extintor Portátil


Punto de Encuentro

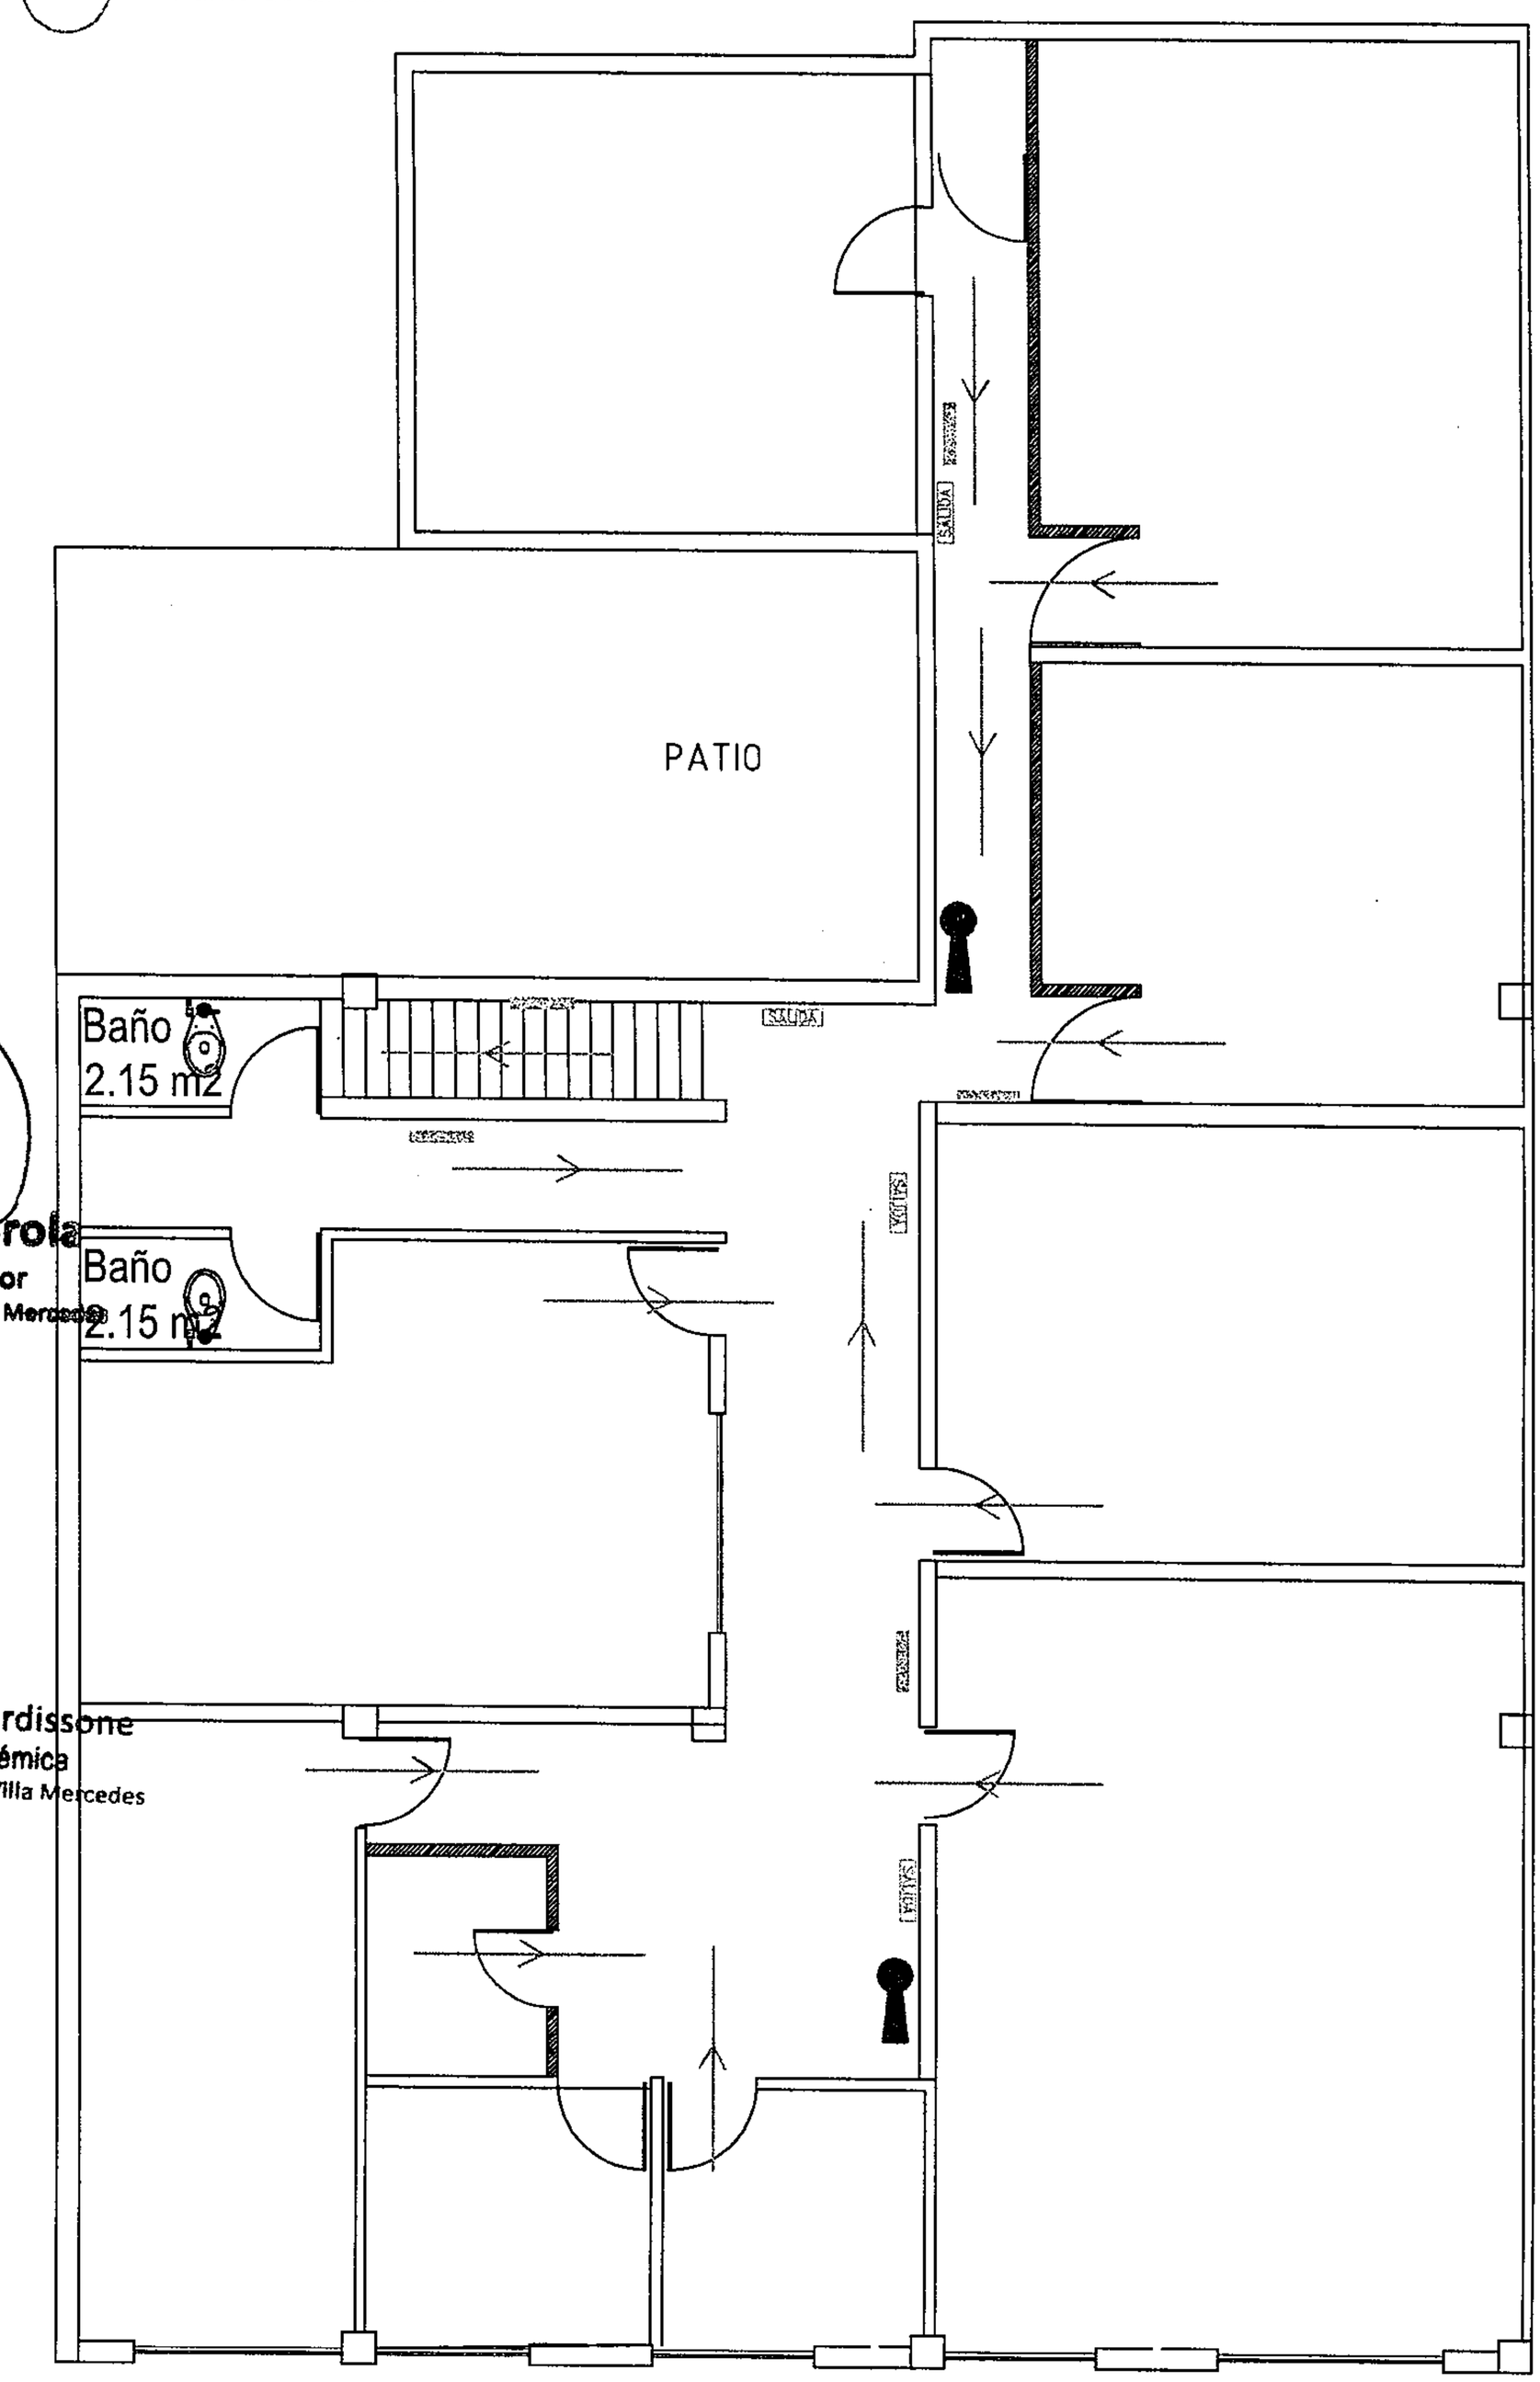

Dr. David Rivarola
Rector Organizador
Universidad Nacional de Villa Mercedes

Daniel Enrique Ardissone
Secretaría Académica
Universidad Nacional de Villa Mercedes

CROQUIS DE EVACUACION - PLANTA BAJA

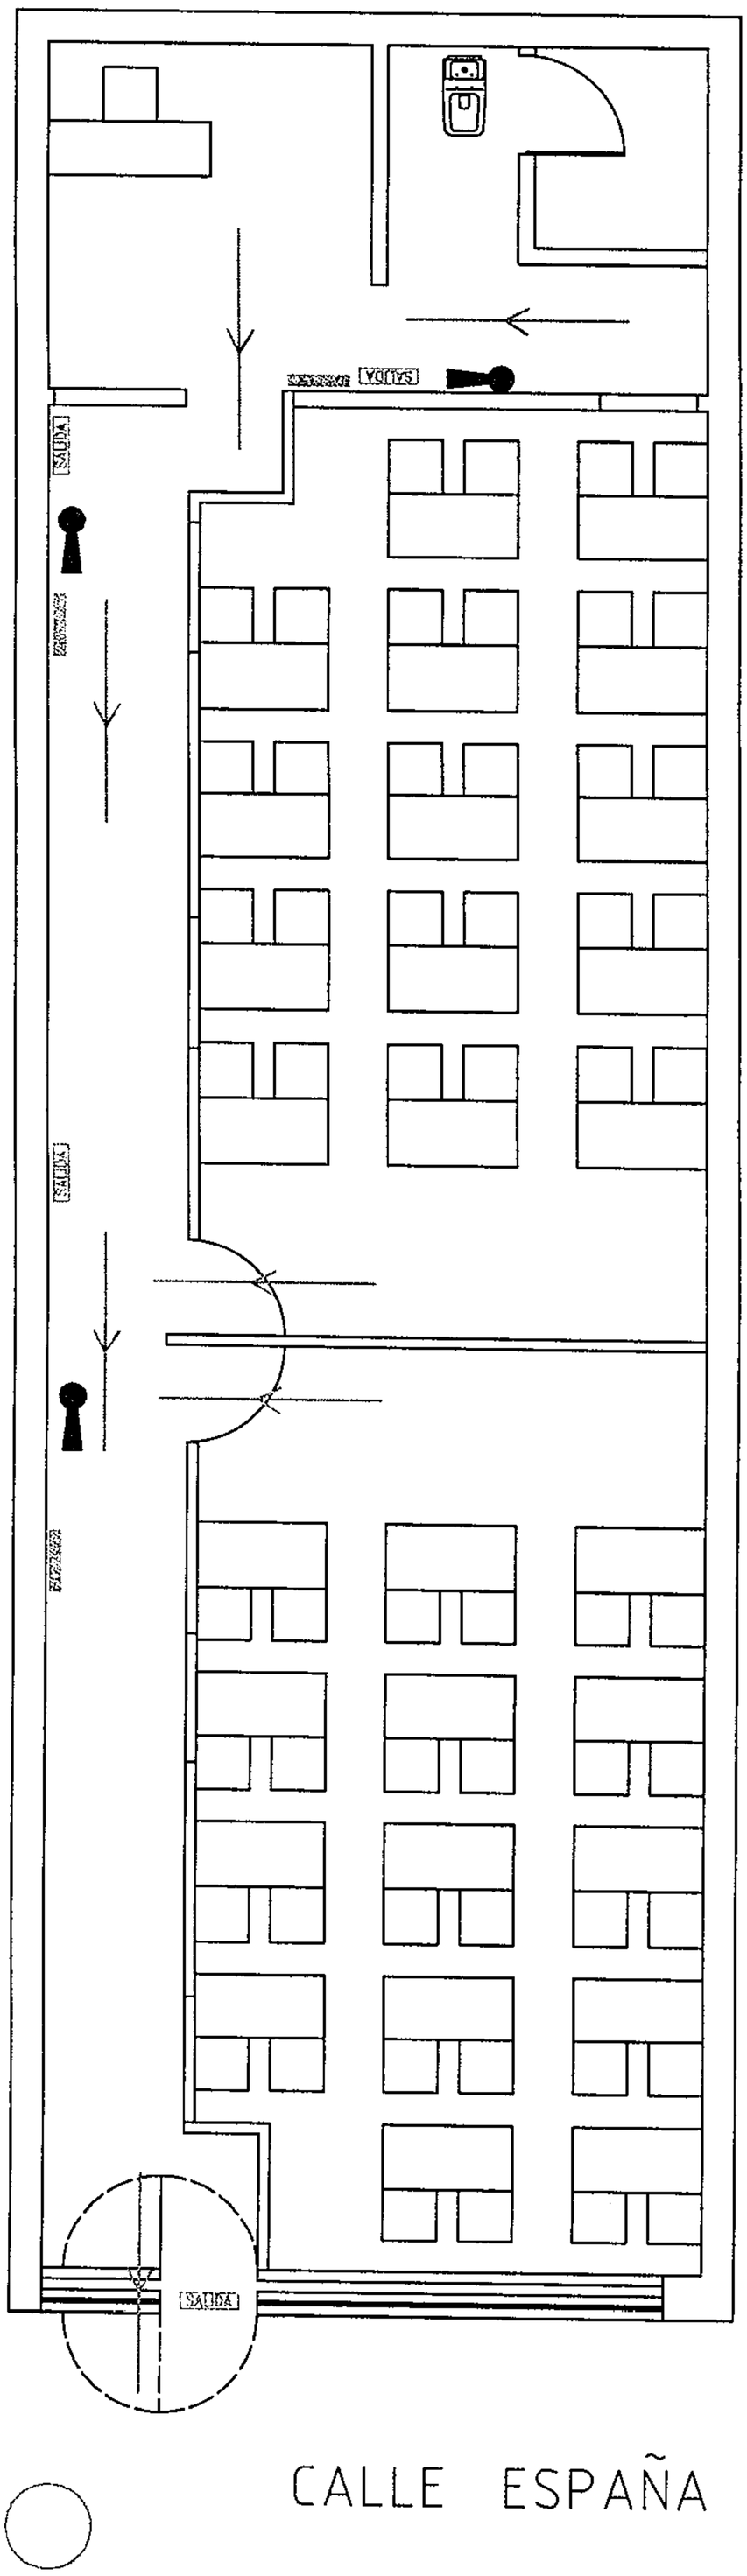

REFERENCIAS

Sentido de la Evacuación


Luces de Emergencias

Extintor Portátil

Punto de Encuentro

Dr. David Rivarola
Rector Organizador
Universidad Nacional de Villa Mercedes

Daniel Enrique Ardissone
Secretaría Académica
Universidad Nacional de Villa Mercedes

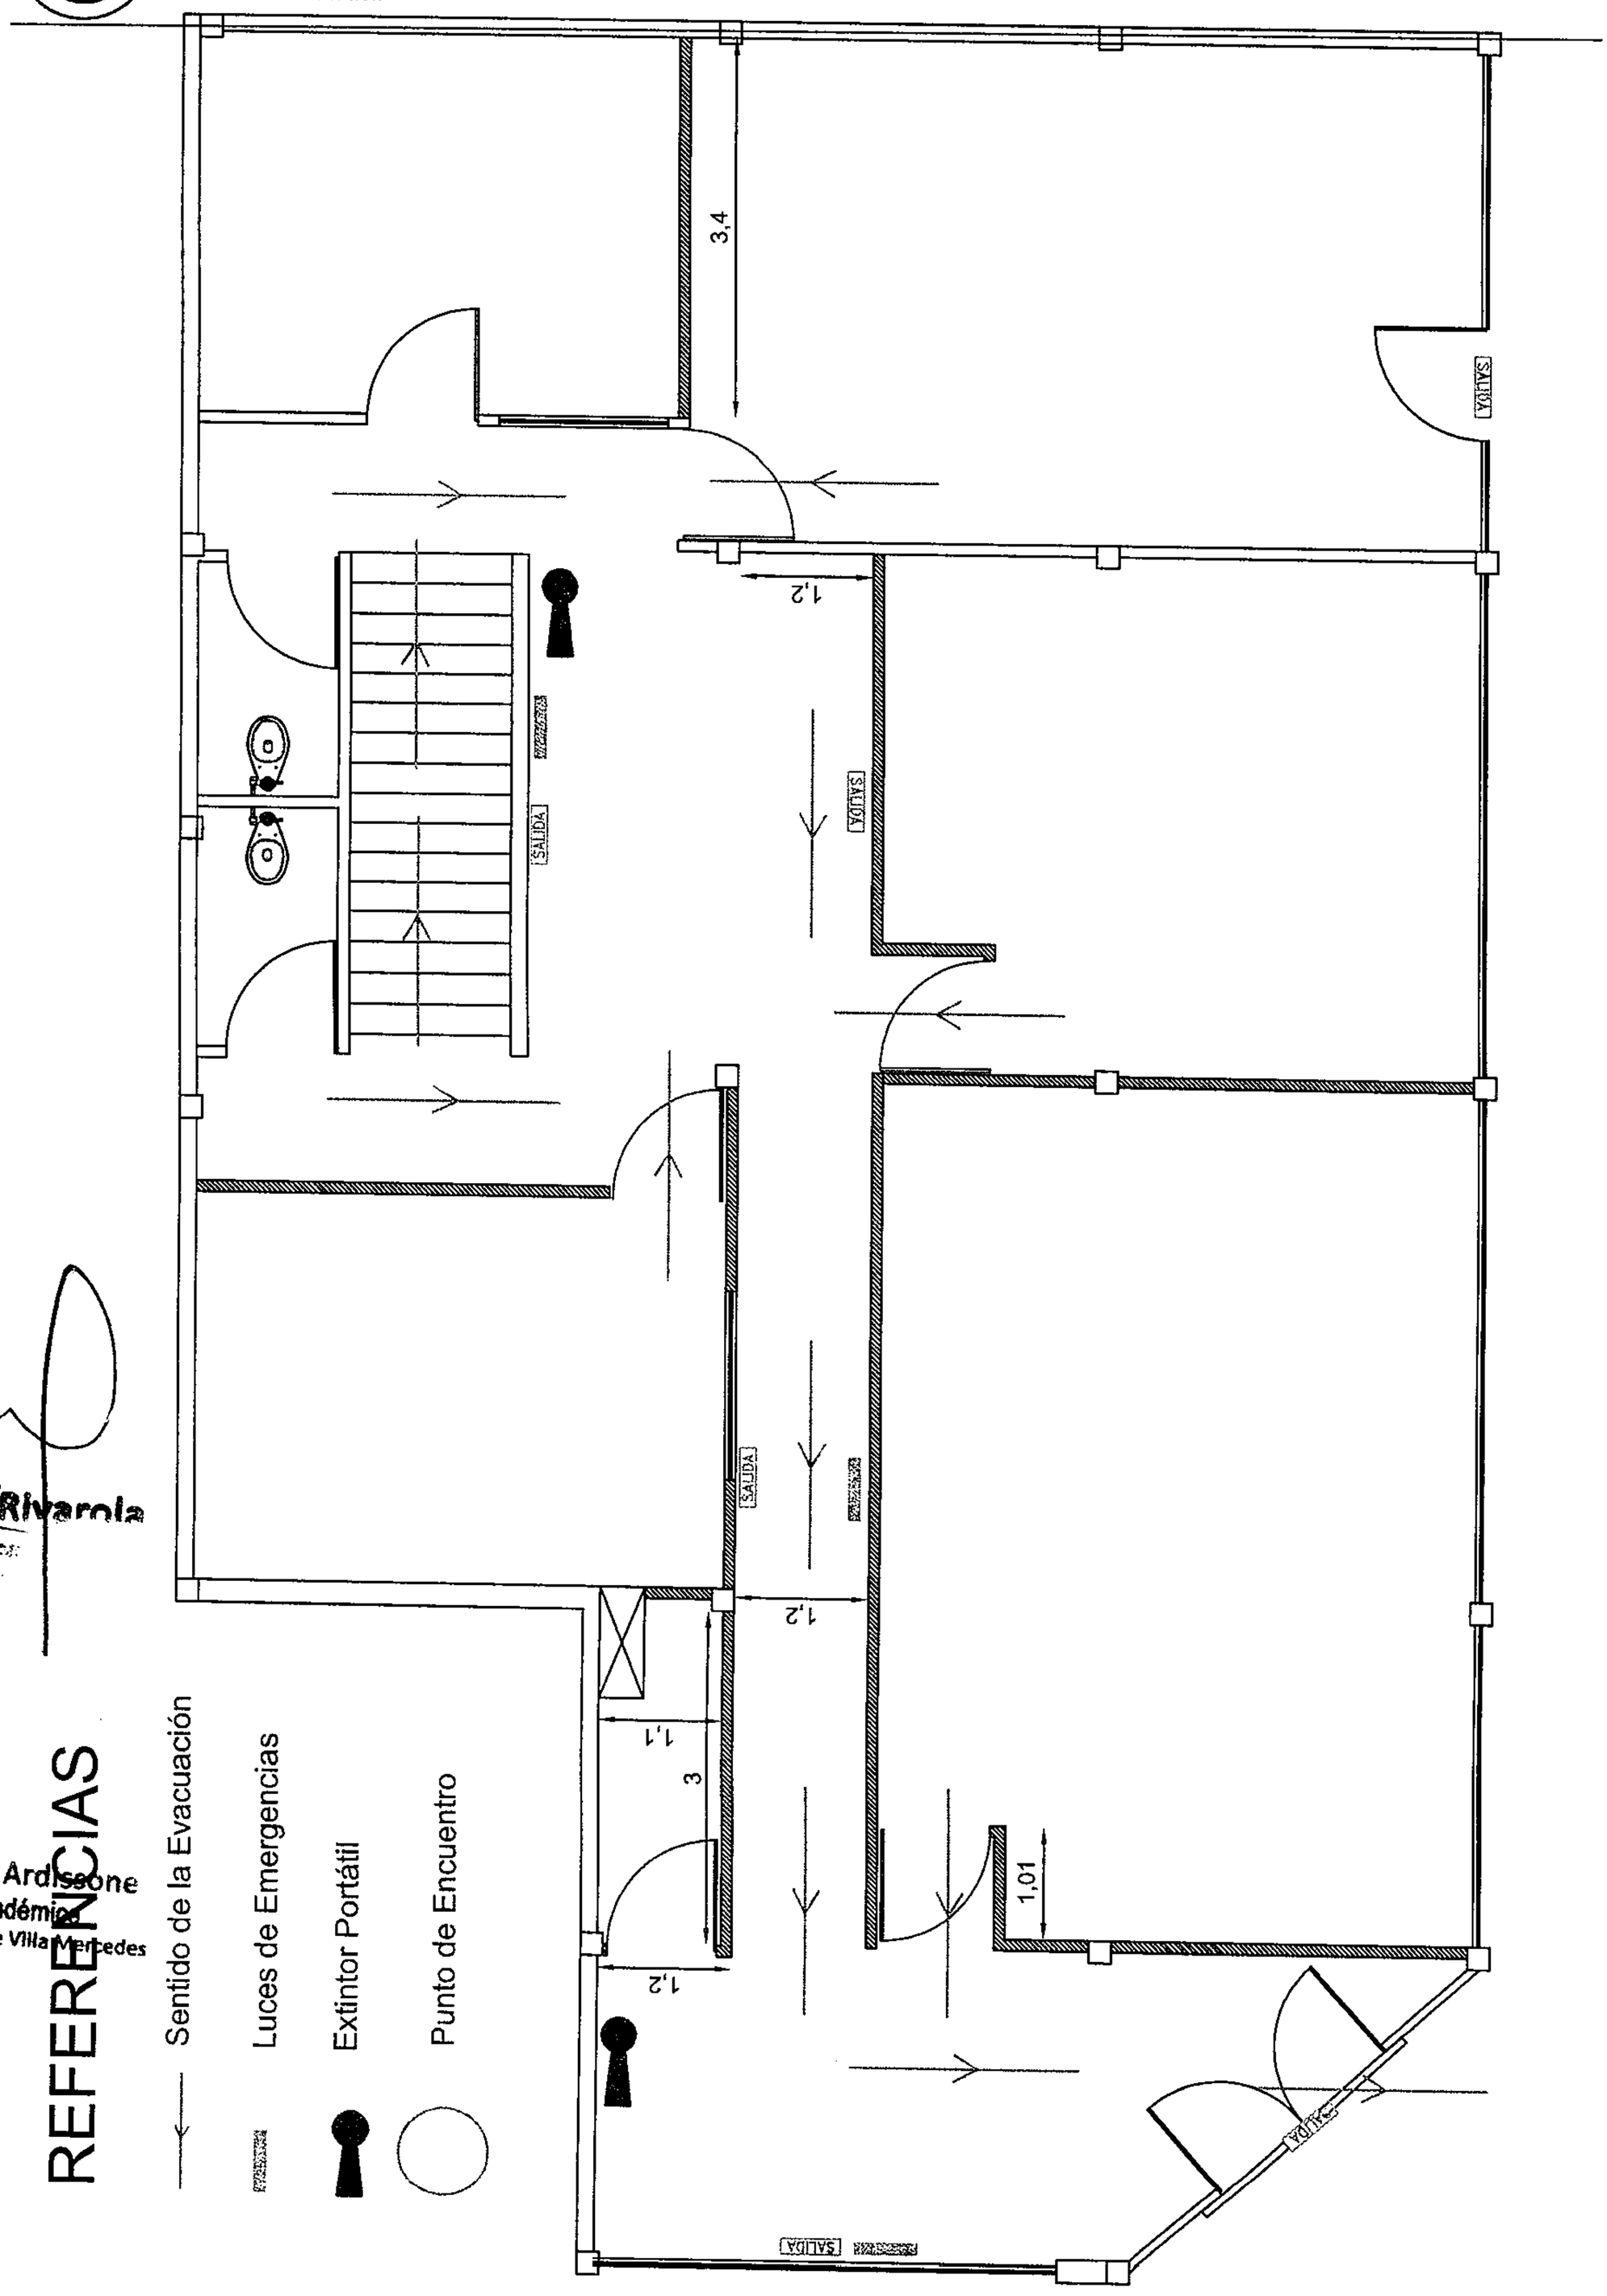

Dr. David Rivarola
Director General

Daniel Enrique Ardissone
Secretaría Académica
Universidad Nacional de Villa Mercedes

CROQUIS DE EVACUACION - PLANTA BAJA


REFERENCIAS

Sentido de la Evacuación

Luces de Emergencias


Extintor Portátil

Punto de Encuentro

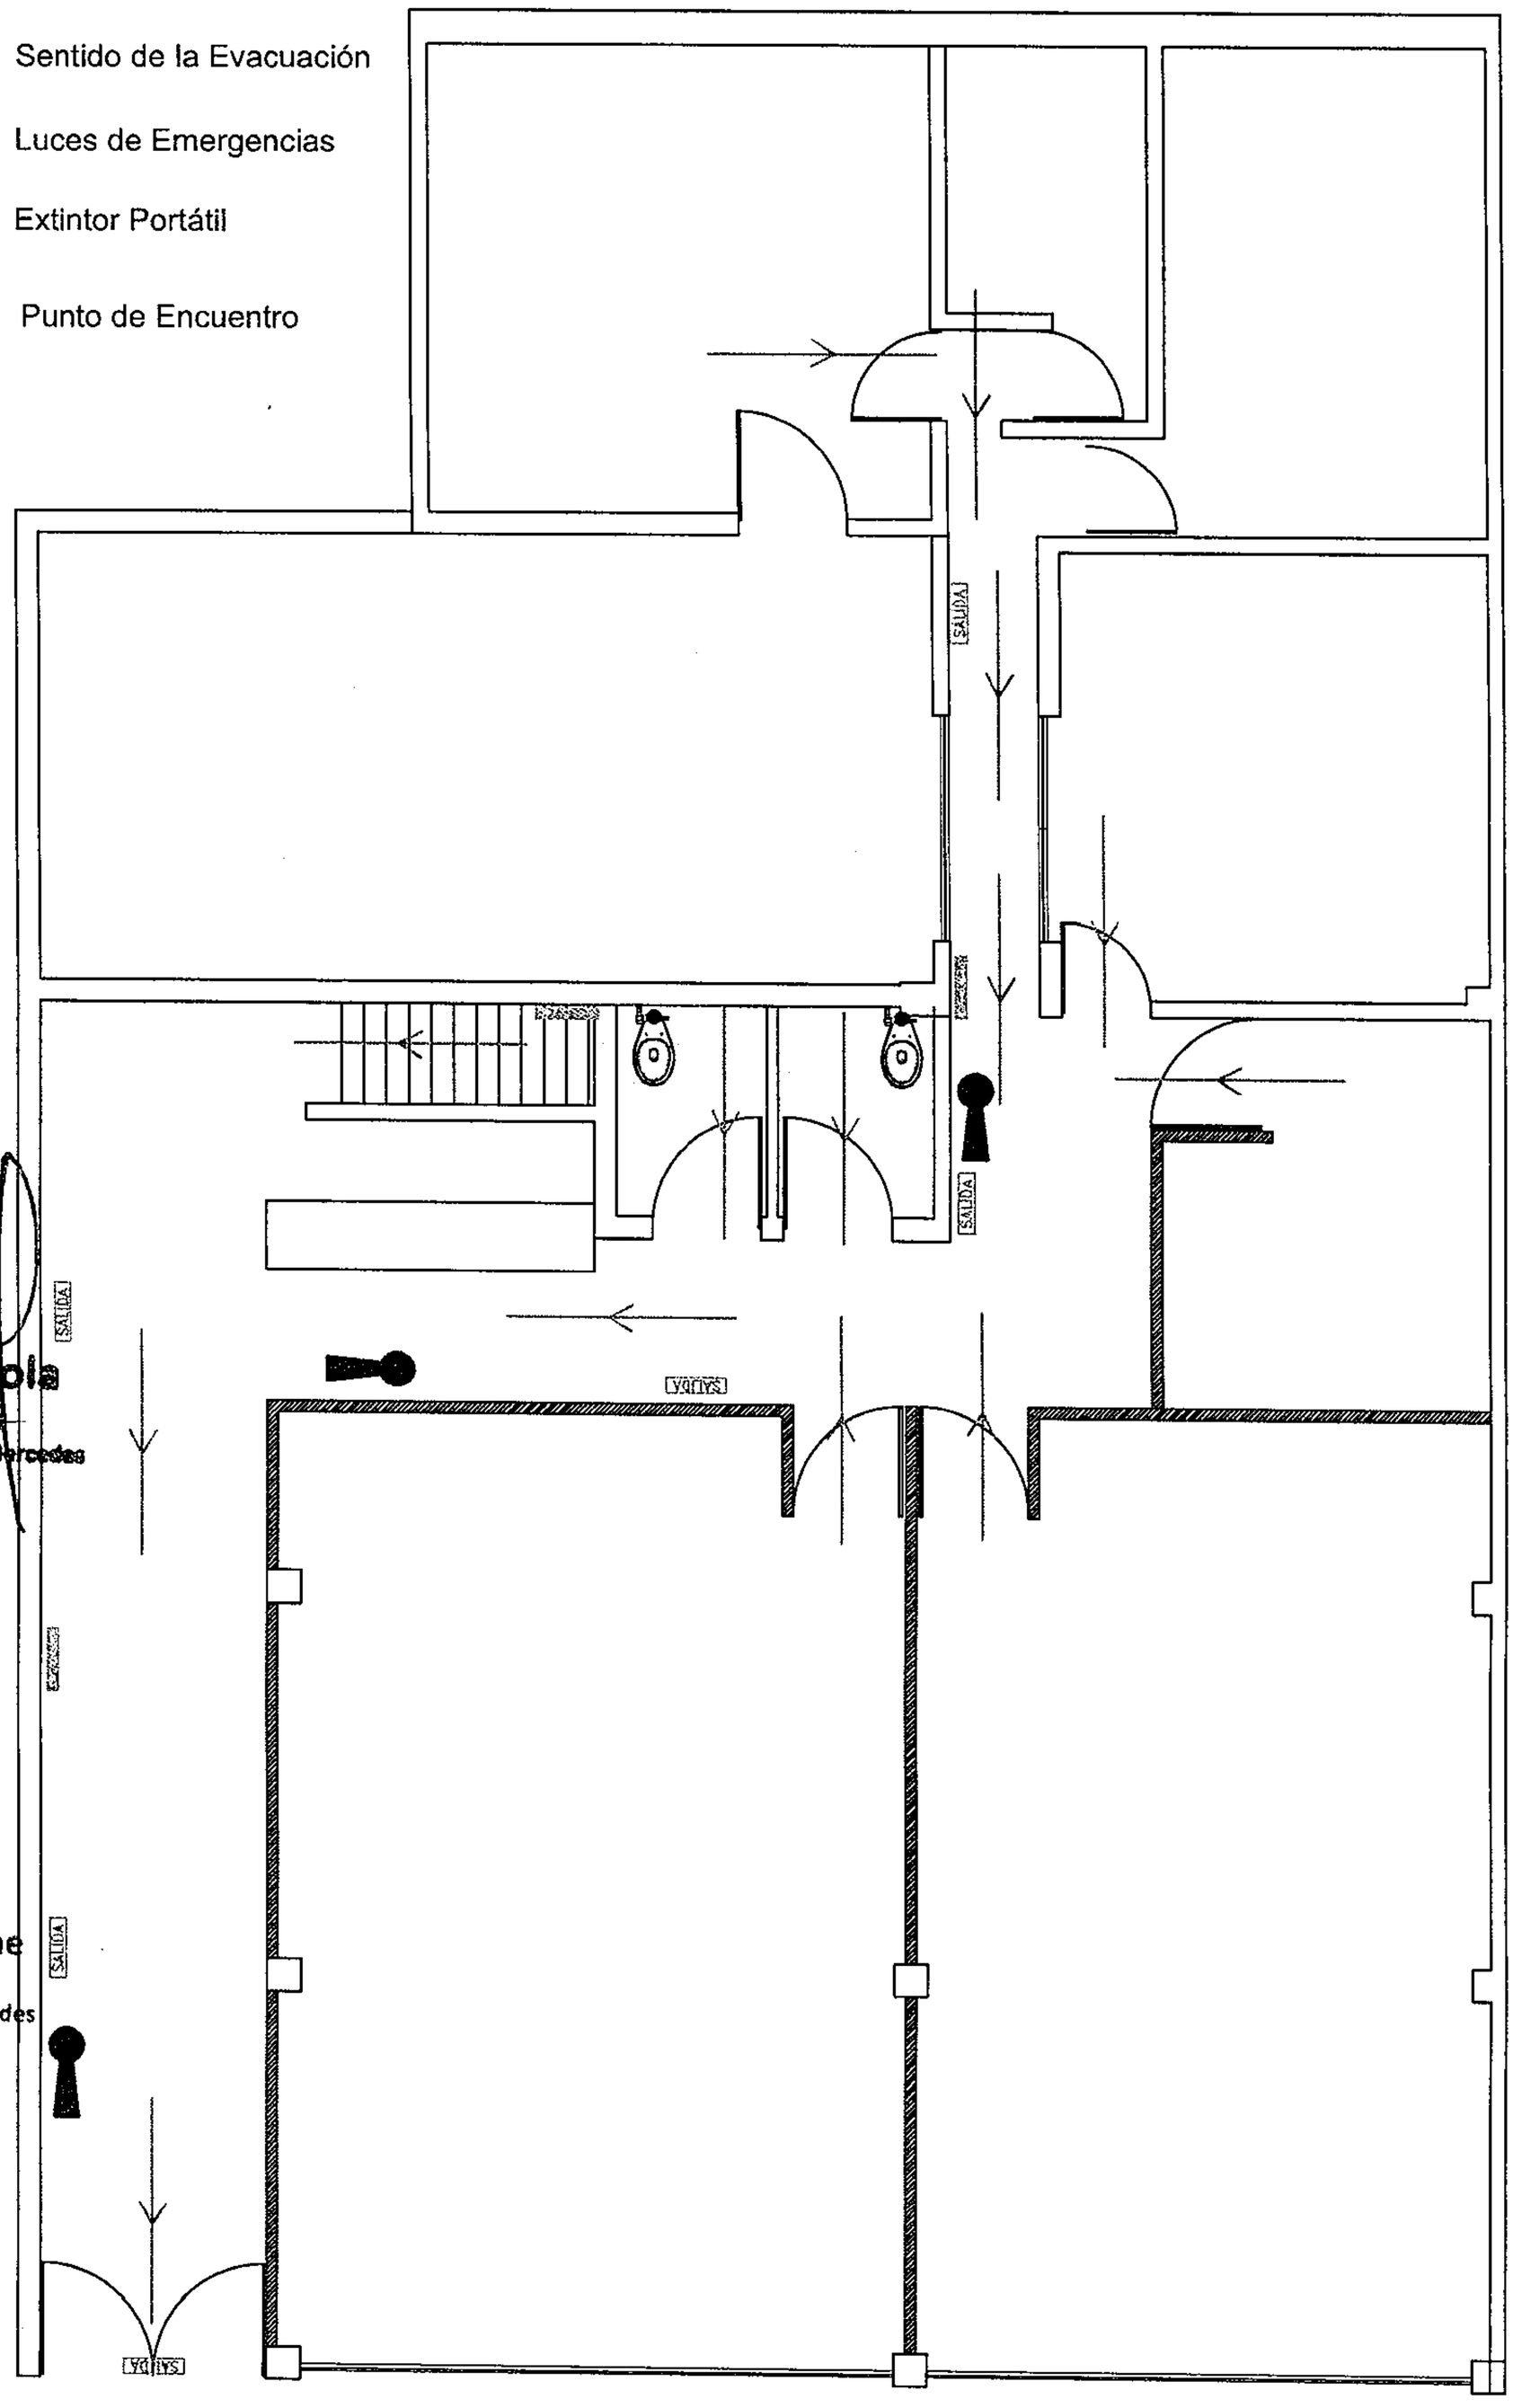

Dr. David Rivarola
Rector Organizador
Universidad Nacional de Villa Mercedes

Daniel Enrique Ardissone
Secretaría Académica
Universidad Nacional de Villa Mercedes

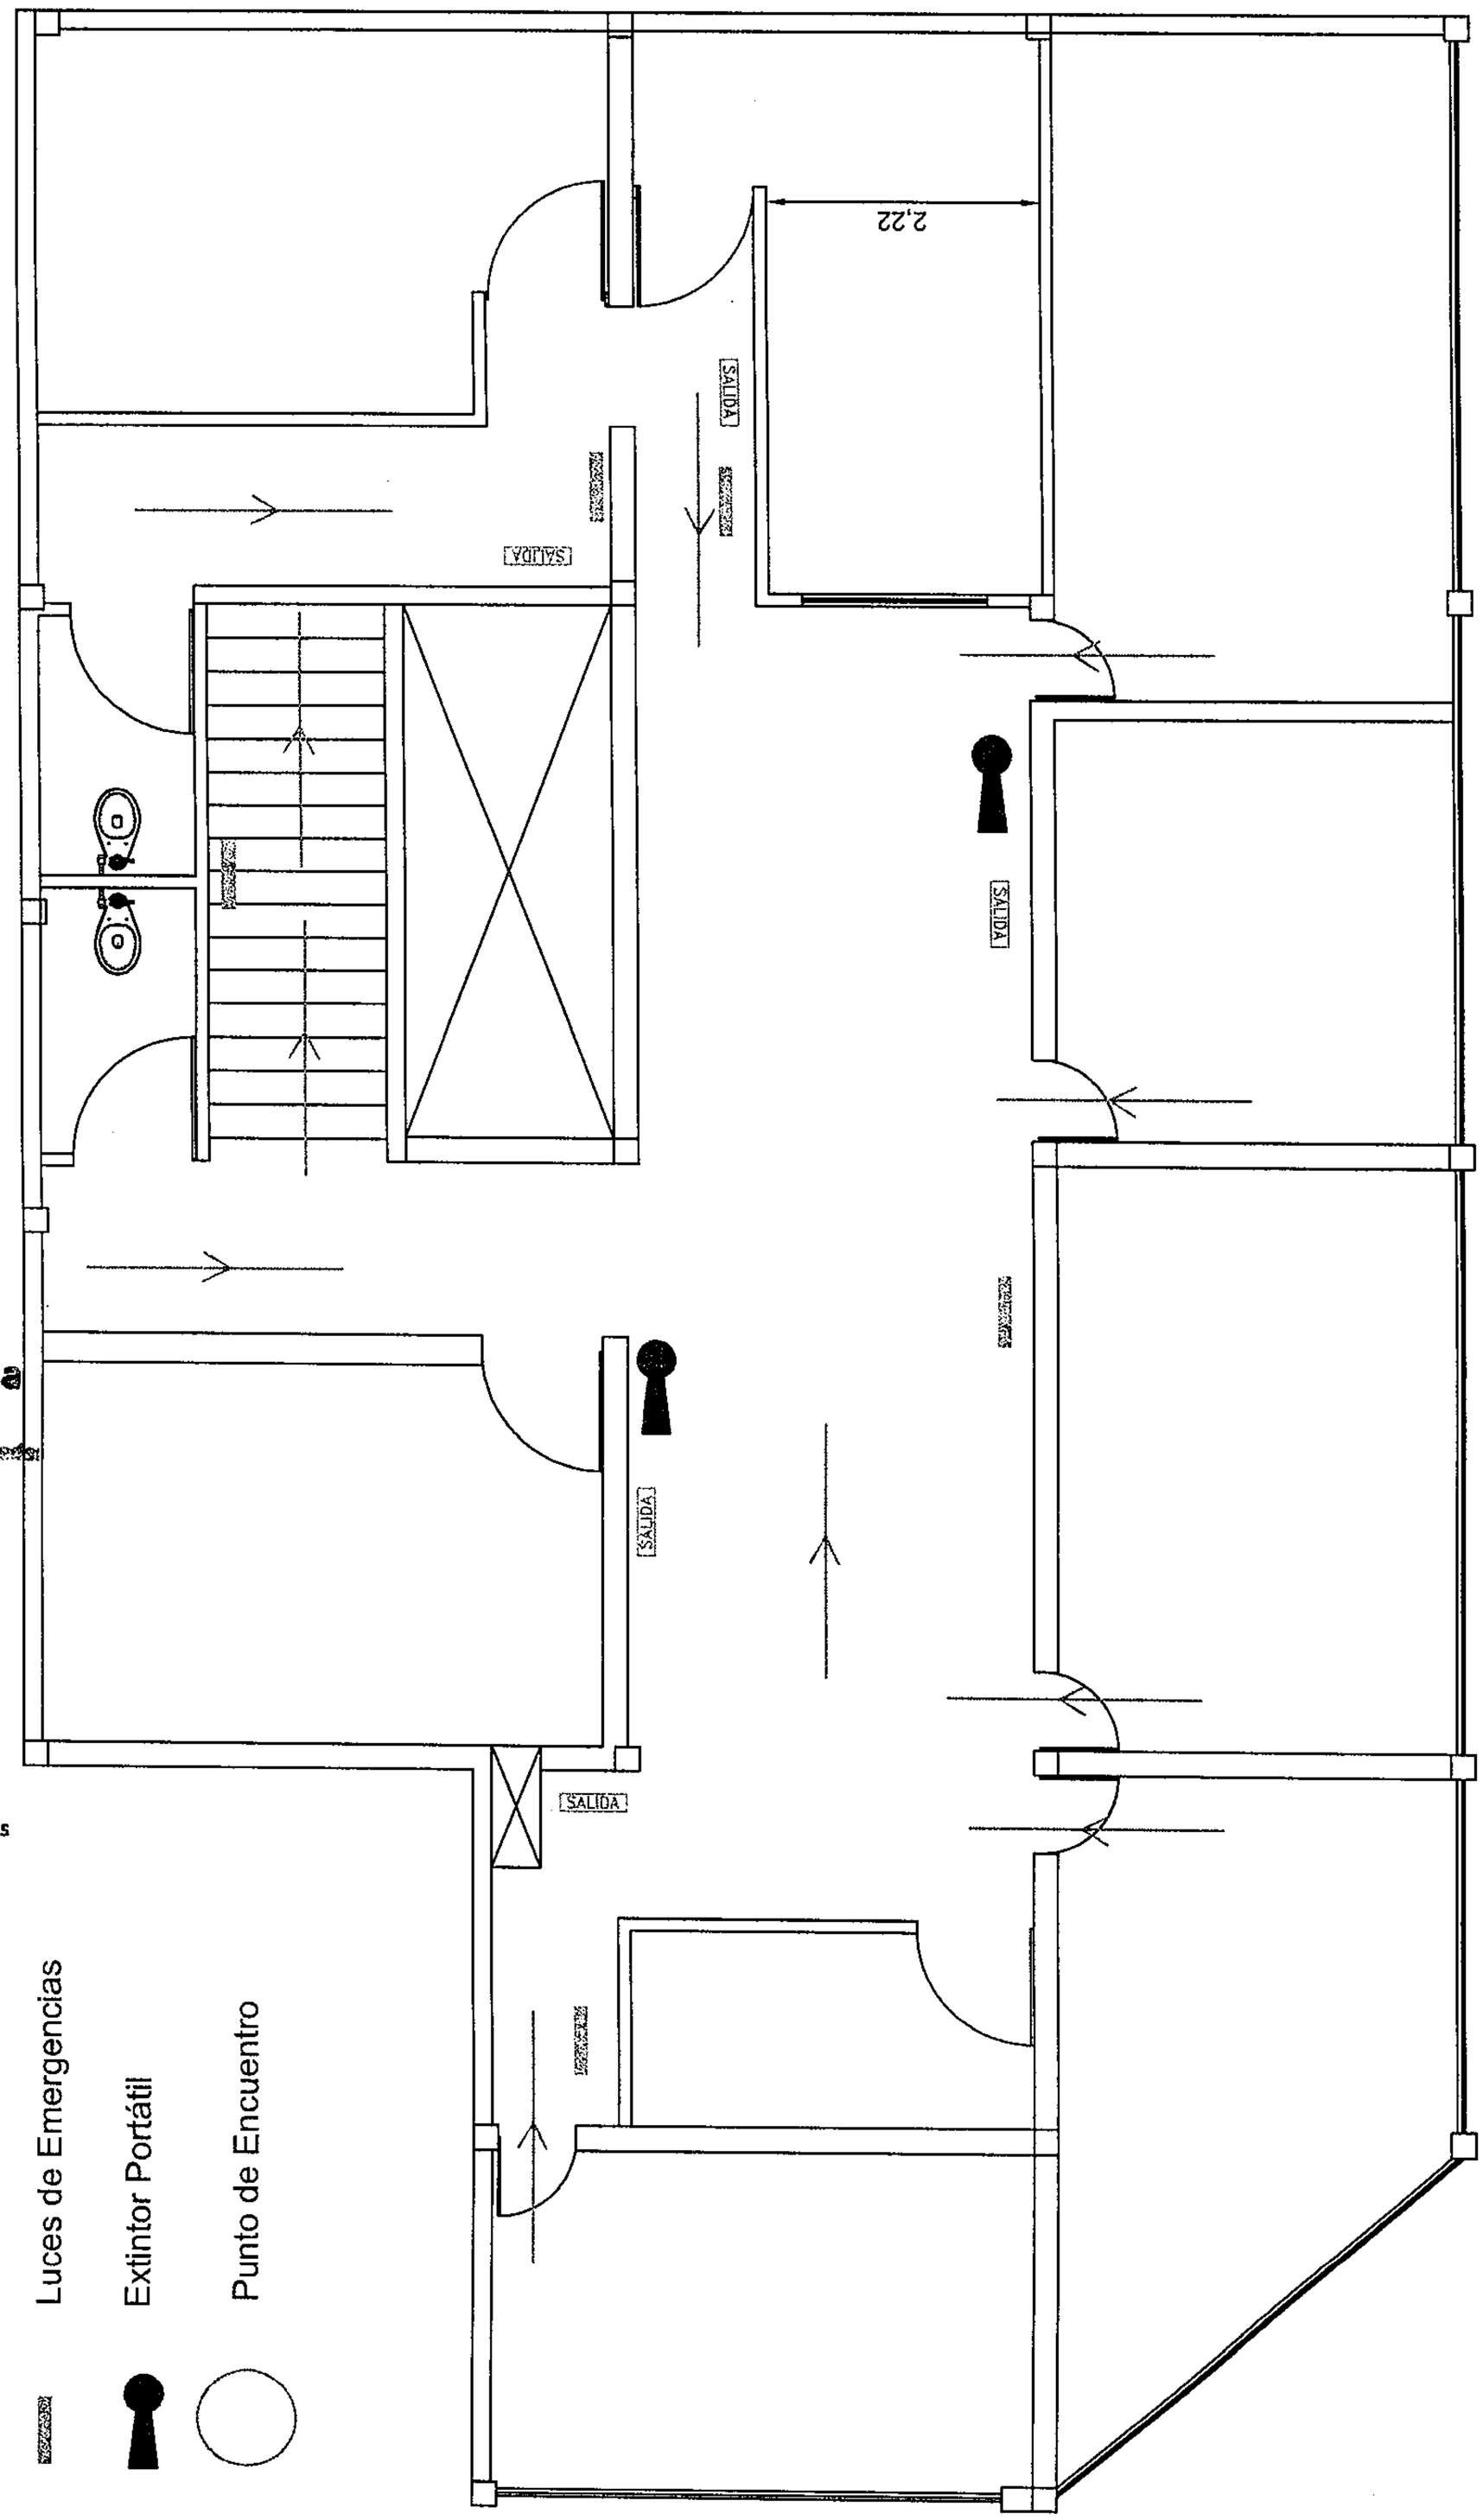

Dr. David Rivarola
Rector Organizador
Universidad Nacional de Villa Mercedes

iel Enrique Ardissone
Secretaría Académica
Universidad Nacional de Villa Mercedes

REFERENCIAS

- Sentido de la Evacuación
- Luces de Emergencias
- Extintor Portátil
- Punto de Encuentro